


Pagrabstāva telpu eksplikācija		
Nr.p.k.	Telpu nosaukums	Platība, m2
0-1	Kāpņu telpa	6.50
0-2	Garderobe	122.31
0-3	WC	17.85
0-4	WC	13.07
0-5	Palīgtelpa	3.33
0-5*	Pagraba telpa	30.09
0-6	Siltummezgls	72.33
0-7	Tehniskā telpa	24.57
0-8	Priekštelpa	15.43
0-9	Tehniskā telpa	170.24
0-10	Priekštelpa	4.78
0-11	Potenciāli elektrosadales telpa	66.00
0-12	Priekštelpa	5.89
0-13	Pagraba telpa	206.72
0-14	Palīgtelpa	6.47
0-15	Priekštelpa	2.95
0-16	Priekštelpa	3.81
0-17	Pagraba telpa	358.29
0-18	Pagraba telpa	33.45

Pagrabstāva telpu eksplikācija		
Nr.p.k.	Telpu nosaukums	Platība, m2
0-20	Priekštelpa	4.99
0-21	Pagraba telpa	581.06
0-22	Priekštelpa	5.06
0-25	Priekštelpa	2.82
0-27	Priekštelpa	2.79
0-28	Priekštelpa	8.42
0-29	Siltummezgls	42.97
0-30	Datu telpa	26.34
		1 839.48 m²

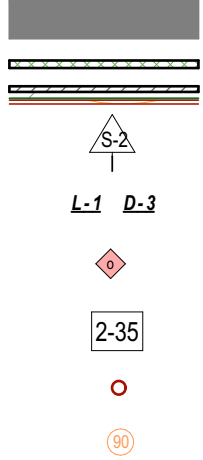


- IZMANTOTIE APZĪMĒJUMI:**
- ESOŠĀ SIENA
 - JAUNBŪVĒJAMA SIENA
 - SIENU MARKA
 - LOGU, DURVJU MARKA
 - DURVJU PIEKĻUVES VIRZIENS
 - TELPU EKSPLIKĀCIJAS NR.
 - VĒDINĀŠANAS KANĀLS
 - AILAS NR.

PIEZĪMES:

- Ēkas plānu skatīt kopā ar griezumiem ARI-10-A, fasādēm AR-8; AR-9, sienu griezumiem ARI-12-A un grīdu griezumiem ARI-13-A; durvju zīmējumiem ARI-16-A līdz ARI-20-A, kā arī ar projekta ARD daļu.
- Visi izmēri doti milimetros, visus izmērus precizēt objektā!
- Zīmējumus nedrīkst mēri! Lasīt rakstītos izmērus!
- Būvuzņēmējs ir atbildīgs par dabā esošo izmēru pārbaudi. Atšķirību gadījumā no projekta risinājuma izmaiņas saskaņot ar projekta autoru. Gadījumā, ja konstatētas atkāpes no projekta, par to nekavējoties jāinformē attiecīgās būvprojekta daļas vadītājs.
- Atsauces uz konkrētiem būvmateriāliem vai piegādātājiem, nozīmē tikai šo būvmateriālu vai piegādājamo pakalpojumu kvalitāti un tehnisko rādītāju nepieciešamību, tie var tikt nomainīti ar ekvivalentiem materiāliem ar līdzvērtīgām tehniskām īpašībām, kas atbilst pastāvošajiem Latvijas standartiem, iepriekš saskaņojot ar attiecīgās būvprojekta sadaļas vadītāju;
- Visas atkāpes no projekta risinājumiem, kā arī no tā izrietošās mezglu un risinājumu papildus detalizācijas izstrādā uzņēmējs, savlaicīgi pirms darbu uzsākšanas vai pasūtījuma izdarīšanas, saskaņojot ar būvprojekta vadītāju un attiecīgās daļas vadītāju.
- Mezglu vai detaļu izgatavošana, kuru detalizācija nav dota projektā, veicama saskaņā ar izgatavotāja norādījumiem un standartshēmām, kā arī normatīvu prasībām.
- * Kāpnes atjaunošanas, izmantojot starp asīm 11 un 12 demontēto kāpņu pakāpienus.

E	16	Maināms kāpņu K-11 novietojums, jo dabā esošās LKT akas novietojums traucē tās izbūvēt.	Indra Valters	20.05.2026.
---	----	---	---------------	-------------

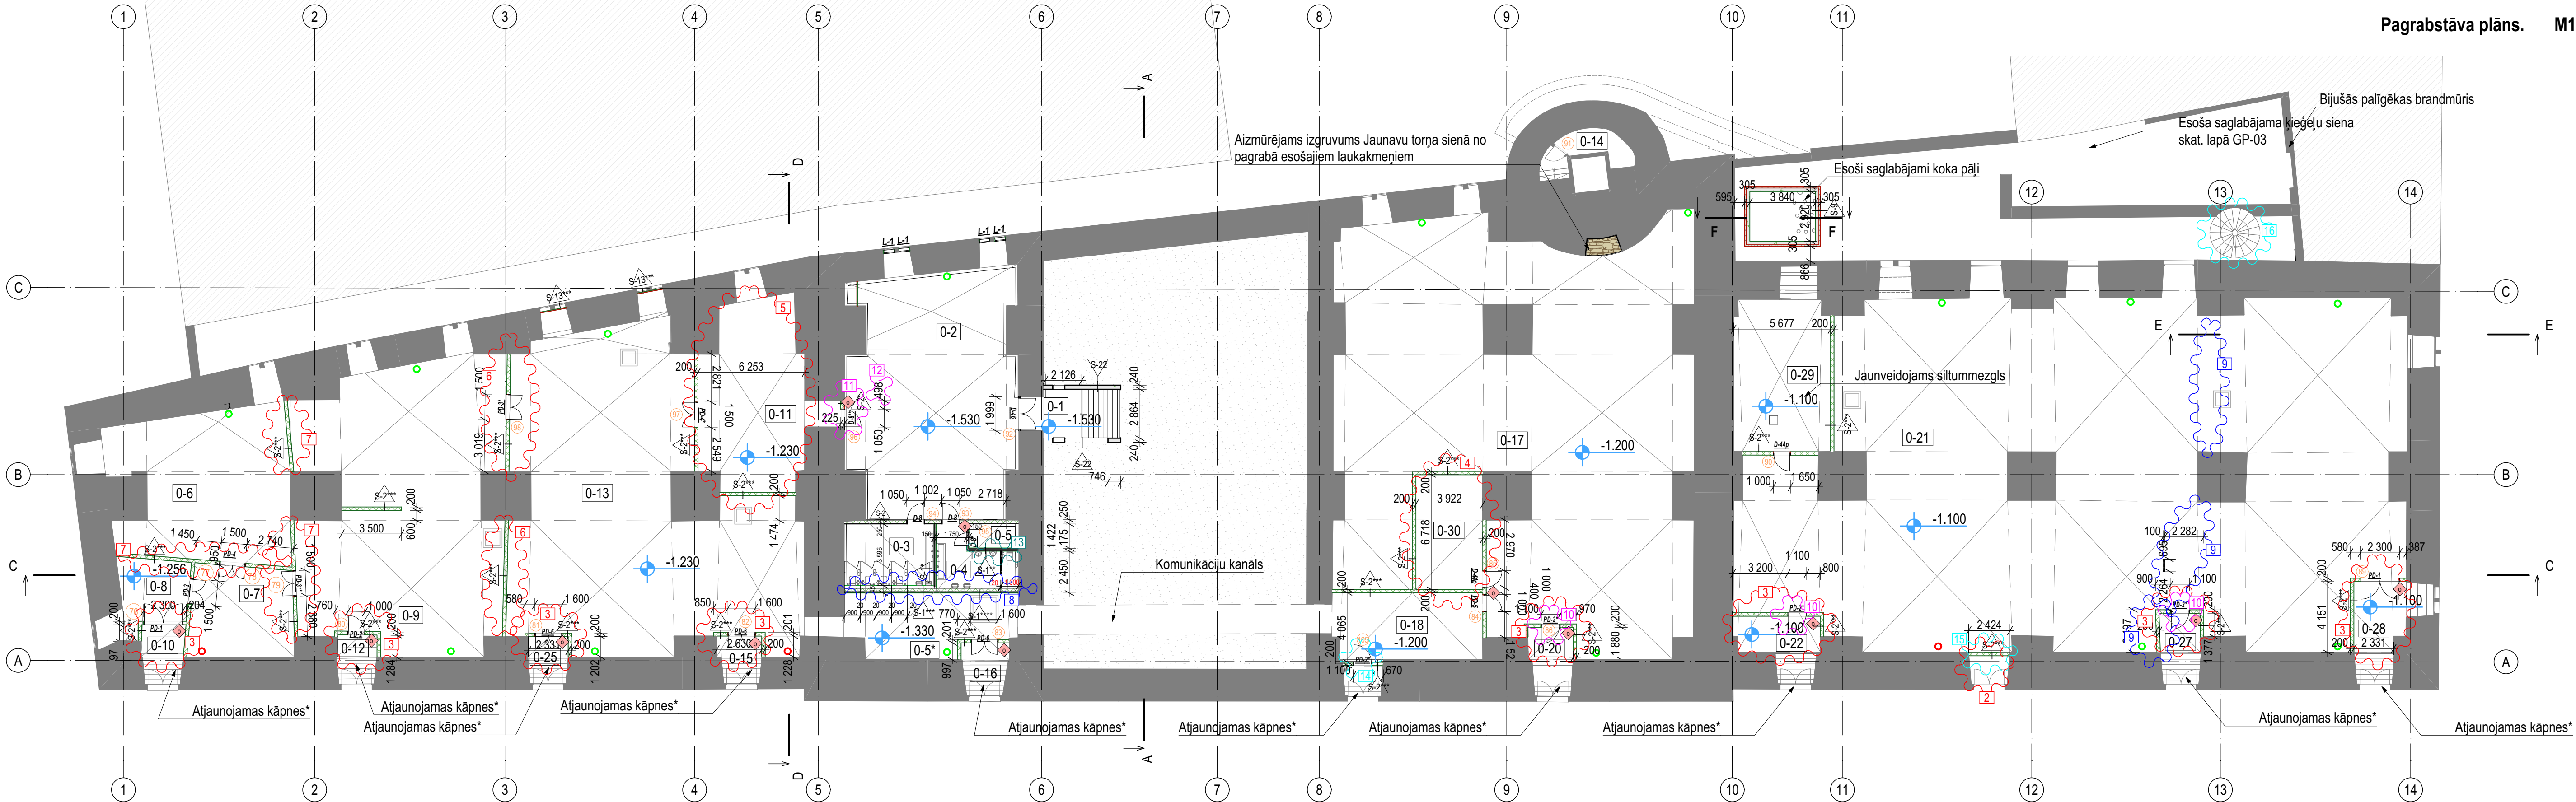

E	15	Mainīts projekta risinājums. Neizbūvējams atkritumu konteiners pacelājs, saskaņā ar LNMM vēstuli 02.07.2026. Nr. 1-8/201. NOS. 2026. izbūvējama siena.	Indra Valters	20.05.2026.
E	14	Labota projekta kļūda. Izbūvējama siena.	Indra Valters	20.05.2026.
D	13	Ierobežotās vietas dēļ, neizbūvējams viens pusuārs.	Indra Valters	02.02.2026.
C	12	Plānoto durvju D-8** aila labotās piesaistes, projektētais ventilācijas caurules dēļ.	Indra Valters	15.12.2025.
C	11	Plānoto durvju D-8** aila, saskaņā ar LNMM 11.11.2025. uzdevumu.	Indra Valters	13.11.2025.
C	10	Labota projekta kļūda. Samazināta durvju PD-2* aila.	Indra Valters	11.11.2025.
B	9	Sienas sliktā tehniskā stāvokļa dēļ (FW, FKA Nr.20), nojaucama siena telpā 0-21, skat. lapā ARI-35-A. Mainās telpas platība.	Indra Valters	27.10.2025.
B	8	Bloku mūris salāgots ar BK daļas kesona biežumu, mainīts mūra biežums no 200mm uz 150mm. Ņemot vērā pagrabā esošos mitruma apstākļus, nomainīta gipskartona sistēma pret fasādes siltinājuma sistēmu.	Indra Valters	18.09.2025.
A	7	Demontējamas sienas, lai izveidotu zemgrīdas hidroizolāciju	Indra Valters	20.06.2025.
A	6	Sienu faktiskā stāvokļa dēļ, sienas demontējamas un izbūvējamas no jauna	Indra Valters	20.05.2025.
A	5	Pasūtītāja uzdevumā, mainīts sadales telpas Nr.0-11 novietojums, platība	Indra Valters	20.05.2025.
A	4	Vietas trūkuma dēļ, mainīts datu telpas Nr.0-30 novietojums, platība	Indra Valters	20.05.2025.
A	3	Saskaņā ar telpu faktiskajiem (velves) izmēriem, mainīts plānojums	Indra Valters	20.05.2025.
A	2	Vietas trūkuma dēļ, mainīta atkritumu konteiners pacelēja vieta	Indra Valters	20.05.2025.
A		Demontāžas apjomi precizēti, izņemti no lapas ARI-2, parādīti jaunveidotā lapā ARI-35	Indra Valters	10.05.2025.

BŪVNIECĪBAS IEROSINĀTĀJS: VAS "VALSTS NEKUSTAMIE ĪPAŠUMI" Talejas iela 1, Rīga, LV - 1026 reģ.nr.40003294758			 VALSTS NEKUSTAMIE ĪPAŠUMI			OBJEKTS: izmaiņas pie būvprojekta IZSTĀŽU ZĀLES "ARSENĀLS" PĀRBŪVES PROJEKTS TORŅA IELĀ 1, RĪGĀ kadastra Nr. 0100 008 0055		
BŪVPROJEKTA IZSTRĀDĀTĀJS:  ARHITEKTU BŪROJS PĒRĀVAS IELA 22, RĪGA, LV-1009 BŪVKOMERSANTA REĢ. NR.: 1026-R REG.NR. 4000345772			DAĻA: ARHITEKTŪRA		MARKA AR			
			RĀSĒJUMA NOSAUKUMS: Pagrabstāva plāns.					
B.P.V. Aldis Polis		03.07.2026	sert.Nr.1-00572	Mērogs 1:200	STADIJA BP			
B.P.D.V. Aldis Polis		03.07.2026	sert.Nr.1-00572	DATUMS 03.07.2026	LAPA ARI-2-E	IZM. E	LAPU SKATĪT	
Arhitekta Elita Pole		03.07.2026	sert.Nr.1-00012					
Arhitekta Indra Valters		03.07.2026	sert.Nr.1-00804					
Arhitekta Laila Ruža		03.07.2026						
Līguma/arhīva Nr. ARS_1.13/2024								