


Fails "Arsenāls" revīzijas: 18.01.2021 15:27

ŠIS RASEJUMS TIEK IZSNIEGTS TIKAI KĀ PROJEKTA DOKUMENTĀCIJAS SASTĀVDAĻA. SAŅĒMĒJIS PIEKĪRT NEPAVIAROTUN. NEIZMAINĪT ŠO RASEJUMU VAI TĀ DAĻAS BEZ PROJEKTĒTĀJA PIKĪRŠANAS. SAŅĒMĒJIS PIEKĪRT, KĀ ŠIS RASEJUMS NAV IZMANTOJAMS CITU OBJEKTU PROJEKTĒŠANAI UN CELTNIECĪBAI BEZ SASKĀŅOŠANAS AR ŠIA "ARH STADIJA".

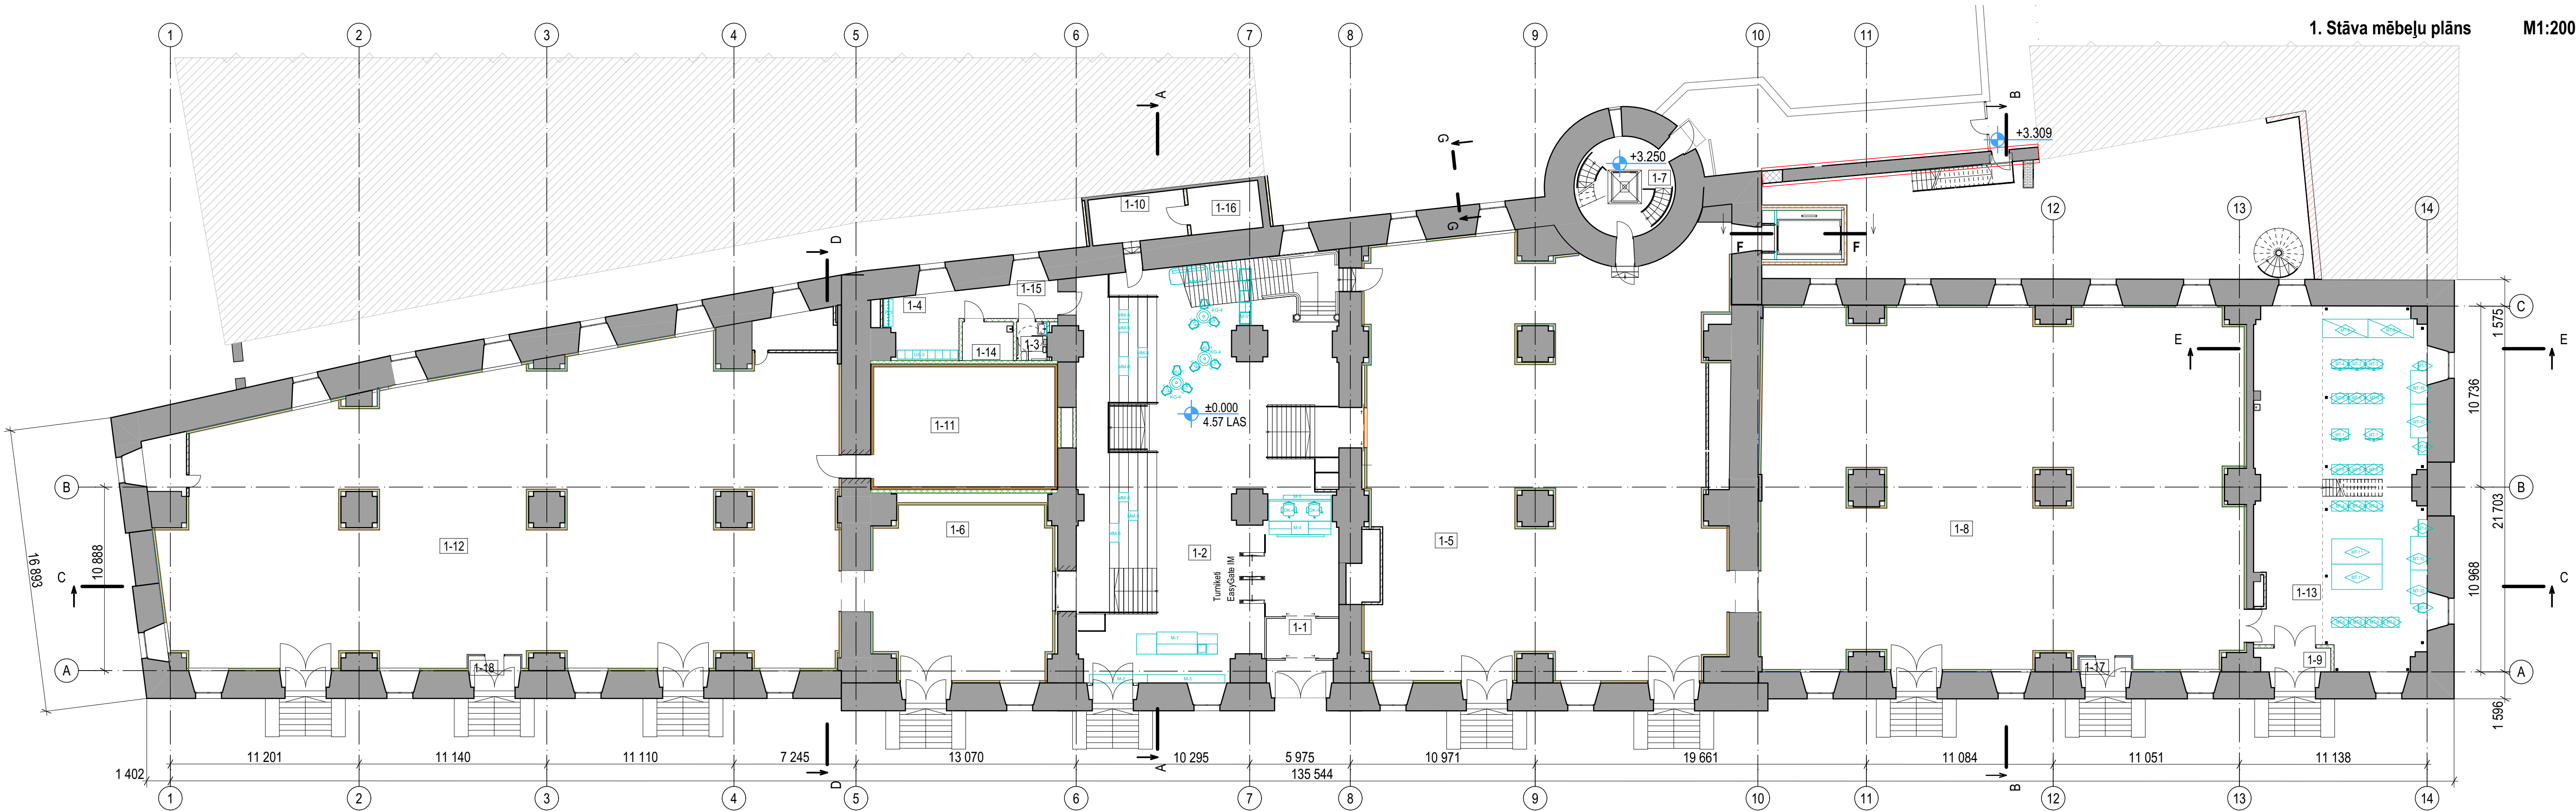

1. Stāva telpu eksplikācija			
Nr.p.k.	Telpu nosaukums	Platība, m2	Grīdas tips
1-1	Vējtveris	18.75	1
1-2	Ieejas vestibils	341.75	4
1-3	Invalidu WC	4.13	6
1-4	Invalidu garderobe	17.55	5
1-5	Izstāžu zāle	543.22	5
1-6	Vestibils	117.57	5
1-7	Kāpņu telpa	24.15	6*/ kājslauķis
1-8	Izstāžu zāle	602.61	5
1-9	Vējtveris	8.38	5**
1-10	Kafejnīcas palīgtelpa	17.02	4**
1-11	Videomākslas telpa	76.01	5*
1-12	Izstāžu zāle	693.87	5
1-13	Pakošanas telpa	1.64	5
1-14	Pakošanas telpa	209.33	5**
1-15	Apkopējas palīgtelpa	6.94	6
1-16	Garderobes priekštelpa	11.63	5
1-17	Elektrosadales telpa	12.36	4**
1-18	Vējtveris	5.16	5**
		4.89	5**
		2 716.95 m²	

- IZMANTOTIE APZĪMĒJUMI:**
- ESOŠĀ SIENA
 - JAUNBŪVĒJAMA SIENA
 - TELPU EKSPLIKĀCIJAS NR.
 - MĒBELES

Piezīmes:

1. Lapu skatīt kopā ar mēbeļu specifikāciju.

BŪVNIECĪBAS IEROSINĀTĀJS: VAS "VALSTS NEKUSTAMIE ĪPAŠUMI" Talejas iela 1, Rīga, LV - 1026 reģ.Nr.40003294758		OBJEKTS: IZSTĀŽU ZĀLES "ARSENĀLS" PĀRBŪVES PROJEKTS TORŅA IELĀ 1, RĪGĀ kadastra Nr. 0100 008 0055	
BŪVPROJEKTA IZSTRĀDĀTĀJS: PS "AD SPATIUM" Vānu iela 22A, Rīga, LV - 1009 reģ.Nr.40003184666, būvkomersanta reģ. Nr. 16303		DAĻA ARHITEKTŪRA	MARKA IN
ATBILDIGĀIS PROJEKTĒTĀJS: ARHSTADIJA ARHITEKTU BŪVĒRIS PĒRŠĀVIS (18.01.2021. RĪGĀ 18.01.2021.) BŪVPROJEKTA REĢ. NR. 16303-9 reģ.Nr.40003457772		1. Stāva mēbeļu plāns	
Līguma/arhiva Nr. IZD/2018/2688 - 1/2019		B.P.V. Aldis Polis 18.01.2021 sert.Nr.1-00572	Mērogs 1:200 DATUMS 18.01.2021
		B.P.D.V. Aldis Polis 18.01.2021 sert.Nr.1-00572	STADIJA BP IN-15 LAPU SKAITS 15/24
		Arhitekts Eiļa Pole 18.01.2021 sert.Nr.1-00012	
		Arhitekts Indra Valters 18.01.2021 sert.Nr.1-00804	
		Arhitekts Laila Ruža 18.01.2021	