


Fails "Arsenāls" revīzijas: 01.07.2021 14:06

ŠIS RASEJUMS TIEK IZSNIEGTS TIKAI KĀ PROJEKTA DOKUMENTĀCIJAS SASTĀVDAĻA. SAŅĒMĒJS PIEKRĪT NEPAVIAROTIN. NEIZMAINĪT ŠO RASEJUMU VAI TĀ DAĻAS BEZ PROJEKTĒTĀJA PIEMĒRŠANAS. SAŅĒMĒJS PIEKRĪT, KĀ ŠIS RASEJUMS NAV IZMANTOJAMS CITU OBJEKTU PROJEKTĒŠANAI UN CELTNĒCĪBAI BEZ SASKANOŠANAS AR ŠIA "ARH STADIJA".

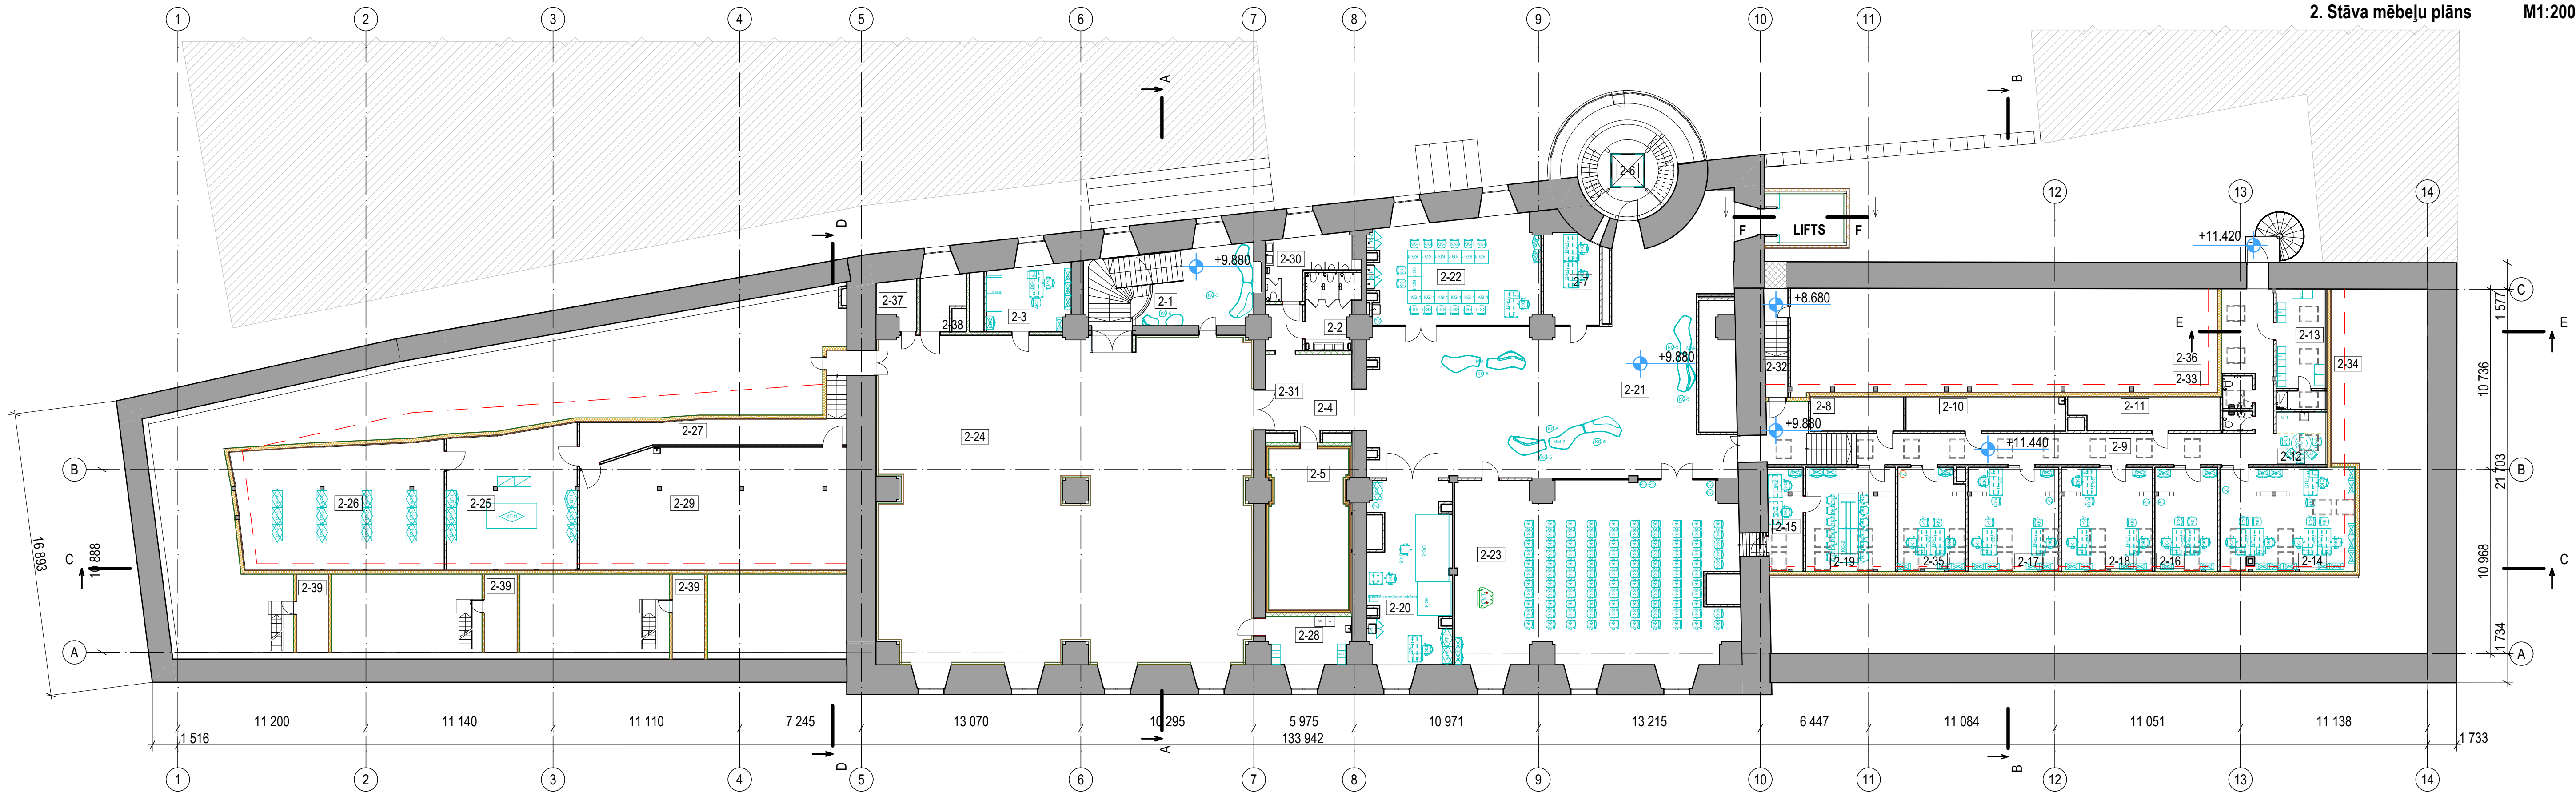

2. Stāva telpu eksplikācija			
Nr.p.k.	Telpu nosaukums	Platība, m2	Grīdas tips
2-1	Kāpņu telpa	32.78	7
2-2	WC	13.56	9
2-3	Vieskuratora darba telpa	20.76	7
2-4	Vestibils	24.11	7
2-5	Videomākslas telpa	44.90	16
2-6	Kāpņu telpa	5.50	6*/ kājslauķis
2-7	Apsardzes palīgtelpa	17.31	7
2-8	Servera telpa	10.35	18
2-9	Gaitenis	74.94	12
2-10	Palīgtelpa	17.71	18
2-11	Palīgtelpa	15.68	18
2-12	Personāla virtuve / atpūtas telpa	3.95	10
2-12	Personāla virtuve / atpūtas telpa	6.19	12
2-13	Darbinieku ēdrtuves	17.66	10
2-14	Darba telpas	34.41	11
2-15	Tulku telpa	10.68	11
2-16	Darba telpas	19.34	11
2-17	Darba telpas + zāles vadītājs	28.02	11
2-18	Darba telpas + ēkas saimnieciskais administrators	28.02	11
2-19	Apspriežu telpa	27.50	11
2-20	Restoratoru telpa	50.84	7*

2. Stāva telpu eksplikācija			
Nr.p.k.	Telpu nosaukums	Platība, m2	Grīdas tips
2-21	Vestibils	220.07	7
2-22	Bērnu nodarbinību telpa	46.60	7
2-23	Konferenču zāle	174.58	16
2-24	Izstāžu telpa	430.93	8
2-25	Palīgtelpa-videotehnikas novietne	63.81	14
2-26	Palīgtelpa - materiālu novietne	88.25	14
2-27	Gaitenis	15.43	14
2-28	Apkopējas palīgtelpa	13.92	9
2-29	Tehniskā telpa	112.71	15
2-30	WC	14.80	9
2-31	Priekštelpa	5.56	7
2-32	Kāpņu telpa	9.00	18
2-33	WC	2.09	10
2-34	Duša	3.30	10
2-35	Darba telpas	24.11	11
2-36	WC	3.48	10
2-37	Datu telpa	5.89	7*
2-38	Palīgtelpa	7.64	7
2-39	Gaisa ierēģšanas telpa	0.00	17
		1 746.38 m²	

- IZMANTOTIE APZĪMĒJUMI:**
- ESOŠĀ SIENA
 - JAUNBŪVĒJAMA SIENA
 - TELPU EKSPLIKĀCIJAS NR.
 - AIZBŪVĒJAMA AILA
 - JUMTA LOGS
 - JUMTA GRIEZUMA LĪNIJA H=1.600
 - MĒBELES

Piezīmes:

1. Lapu skatīt kopā ar mēbeļu specifikāciju.

BŪVNIECĪBAS IEROSINĀTĀJS: VAS "VALSTS NEKUSTAMIE ĪPAŠUMI" Talejas iela 1, Rīga, LV - 1026 reģ.Nr.40003294758		OBJEKTS: IZSTĀŽU ZĀLES "ARSENĀLS" PĀRBŪVES PROJEKTS TORŅA IELĀ 1, RĪGĀ kadastra Nr. 0100 008 0055	
BŪVPROJEKTA IZSTRĀDĀTĀJS: PS "AD SPATIUM" Vānu iela 22A, Rīga, LV - 1009 reģ.Nr.40003184666, būvkomersanta reģ. Nr. 16303		DAĻA ARHITEKTŪRA	MARKA IN
ATBILDIGĀIS PROJEKTĒTĀJS: ARHSTADIJA ARHITEKTU BŪVĒS PĒRŠANAS IELĀ 22, RĪGĀ LV-1009 BŪVPROJEKTA REģ. NR. - 16303-9 reģ.Nr.40003457772		RASEJUMA NOSAUKUMS: 2. Stāva mēbeļu plāns	
Līguma/arhiva Nr. IZD/2018/2688 - 1/2019		B.P.V. Aldis Polis B.P.D.V. Aldis Polis Arhitekts Eiļa Pole Arhitekts Indra Valtere Arhitekts Laila Ruža	01.07.2021 01.07.2021 01.07.2021 01.07.2021 01.07.2021
		sert.Nr.1-00572 sert.Nr.1-00572 sert.Nr.1-00012 sert.Nr.1-00804	Mērogs 1:200 DATUMS 01.07.2021 LAPĀ IN-17 LAPU SKAITS 17/24