


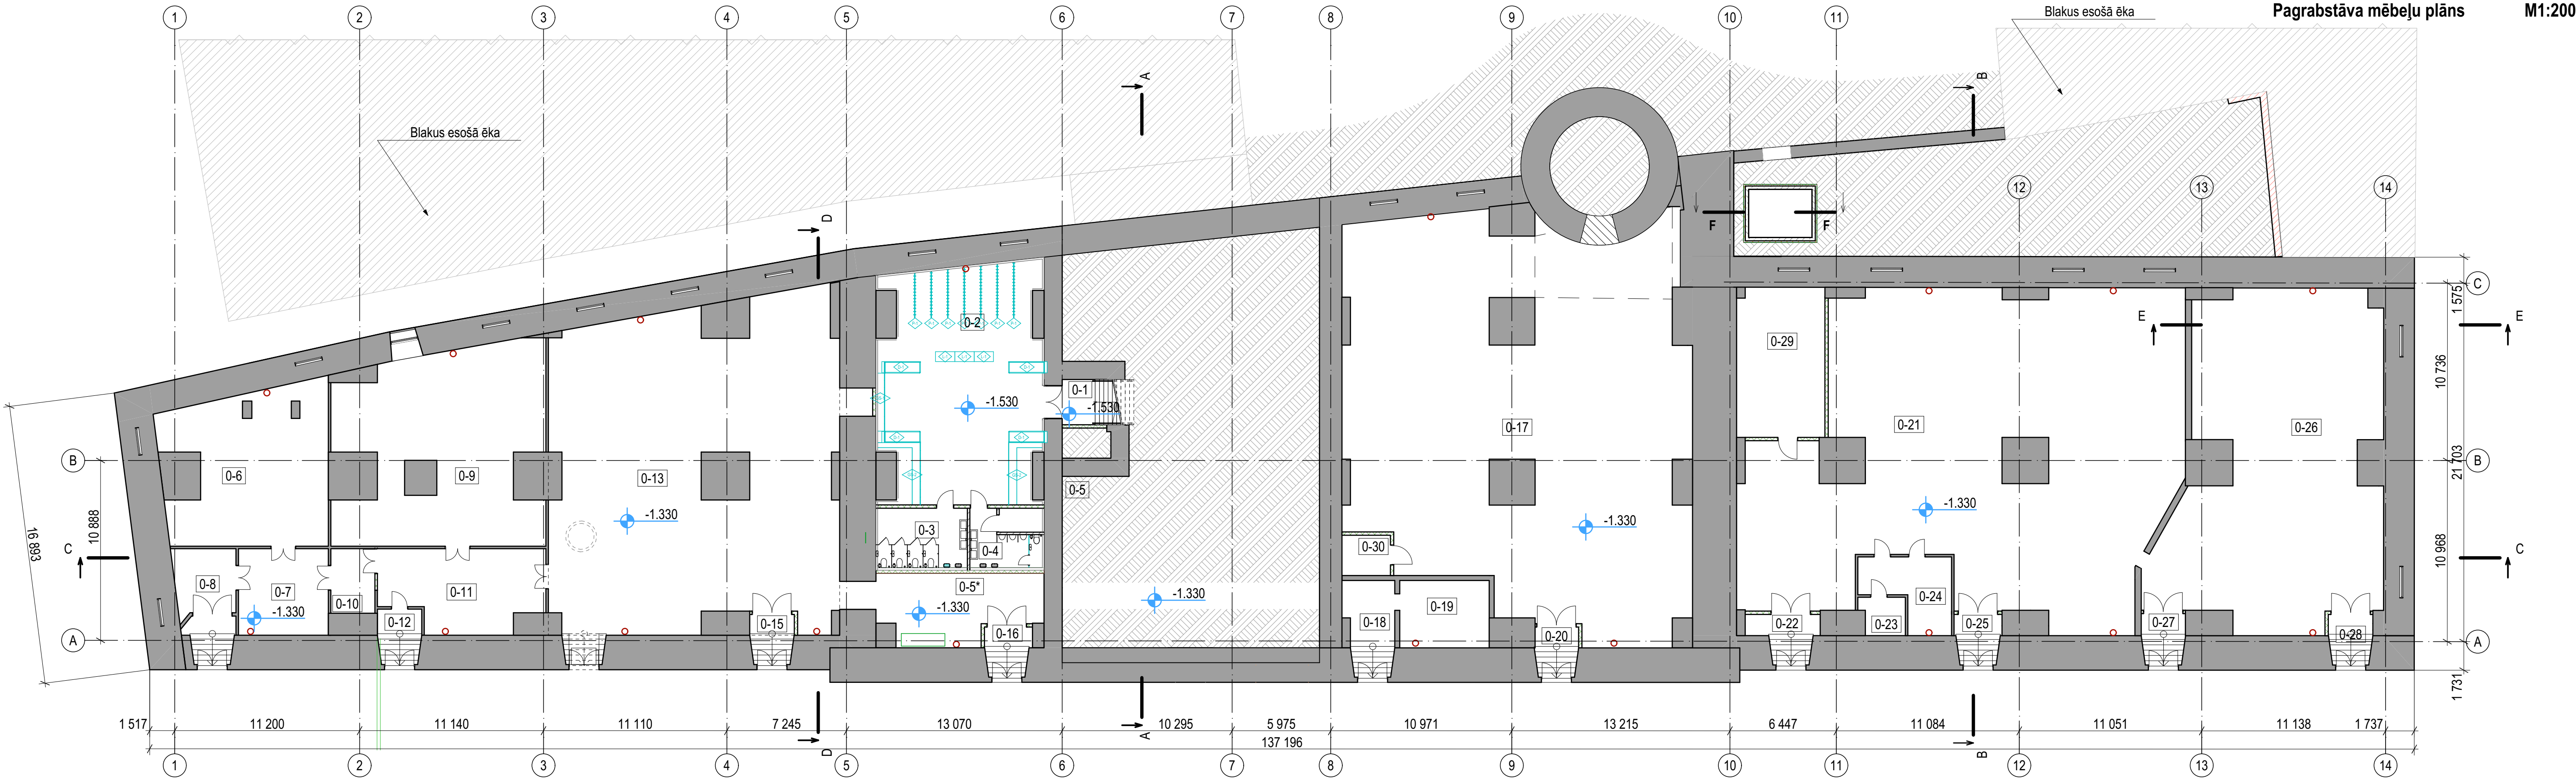

Pagrabstāva telpu eksplikācija				
Nr.p.k.	Telpu nosaukums	Platība, m2	Grīdas tips	
0-1	Kāpņu telpa	5.48	2	
0-2	Garderobe	101.90	2	
0-3	WC	17.85	2	
0-4	WC	11.59	2	
0-5	Palīgtelpa	1.98	2	
0-5*	Tehniskā telpa	28.63	3	
0-6	Siltumapgāde	62.41	3	
0-7	Tehniskā telpa	23.38	3	
0-8	Priekštelpa	14.13	3	
0-9	Pagrabā telpa	89.77	3	
0-10	Pagrabā telpa	5.88	3	
0-11	Tehniskā telpa	34.93	3	
0-12	Pagrabā telpa	0.89	3	
0-13	Pagrabā telpa	218.41	3	
0-15	Priekštelpa	1.98	3	
0-16	Priekštelpa	3.67	3	
0-17	Pagrabā telpa	316.25	3	
0-18	Pagrabā telpa	5.23	3	
0-19	Pagrabā telpa	15.23	3	
0-20	Priekštelpa	0.69	3	
0-21	Pagrabā telpa	431.17	3	

Pagrabstāva telpu eksplikācija				
Nr.p.k.	Telpu nosaukums	Platība, m2	Grīdas tips	
0-22	Priekštelpa	5.84	3	
0-23	Pagrabā telpa	0.86	3	
0-24	Pagrabā telpa	17.70	3	
0-25	Priekštelpa	0.97	3	
0-26	Pagrabā telpa	175.33	3	
0-27	Priekštelpa	0.70	3	
0-28	Priekštelpa	1.22	3	
0-29	Siltummezgls	36.17	3	
0-30	Datu telpa	7.16	3	
		1 637.44 m²		

- ESOŠĀ SIENA
- JAUNBŪVĒJAMA SIENA
- TELPU EKSPLIKĀCIJAS NR.
- MĒBELES

IZMANTOTIE APZĪMĒJUMI:

Piezīmes:

1. Lapu skatīt kopā ar mēbeļu specifikāciju.