
2. Stāva plāns

M1:200

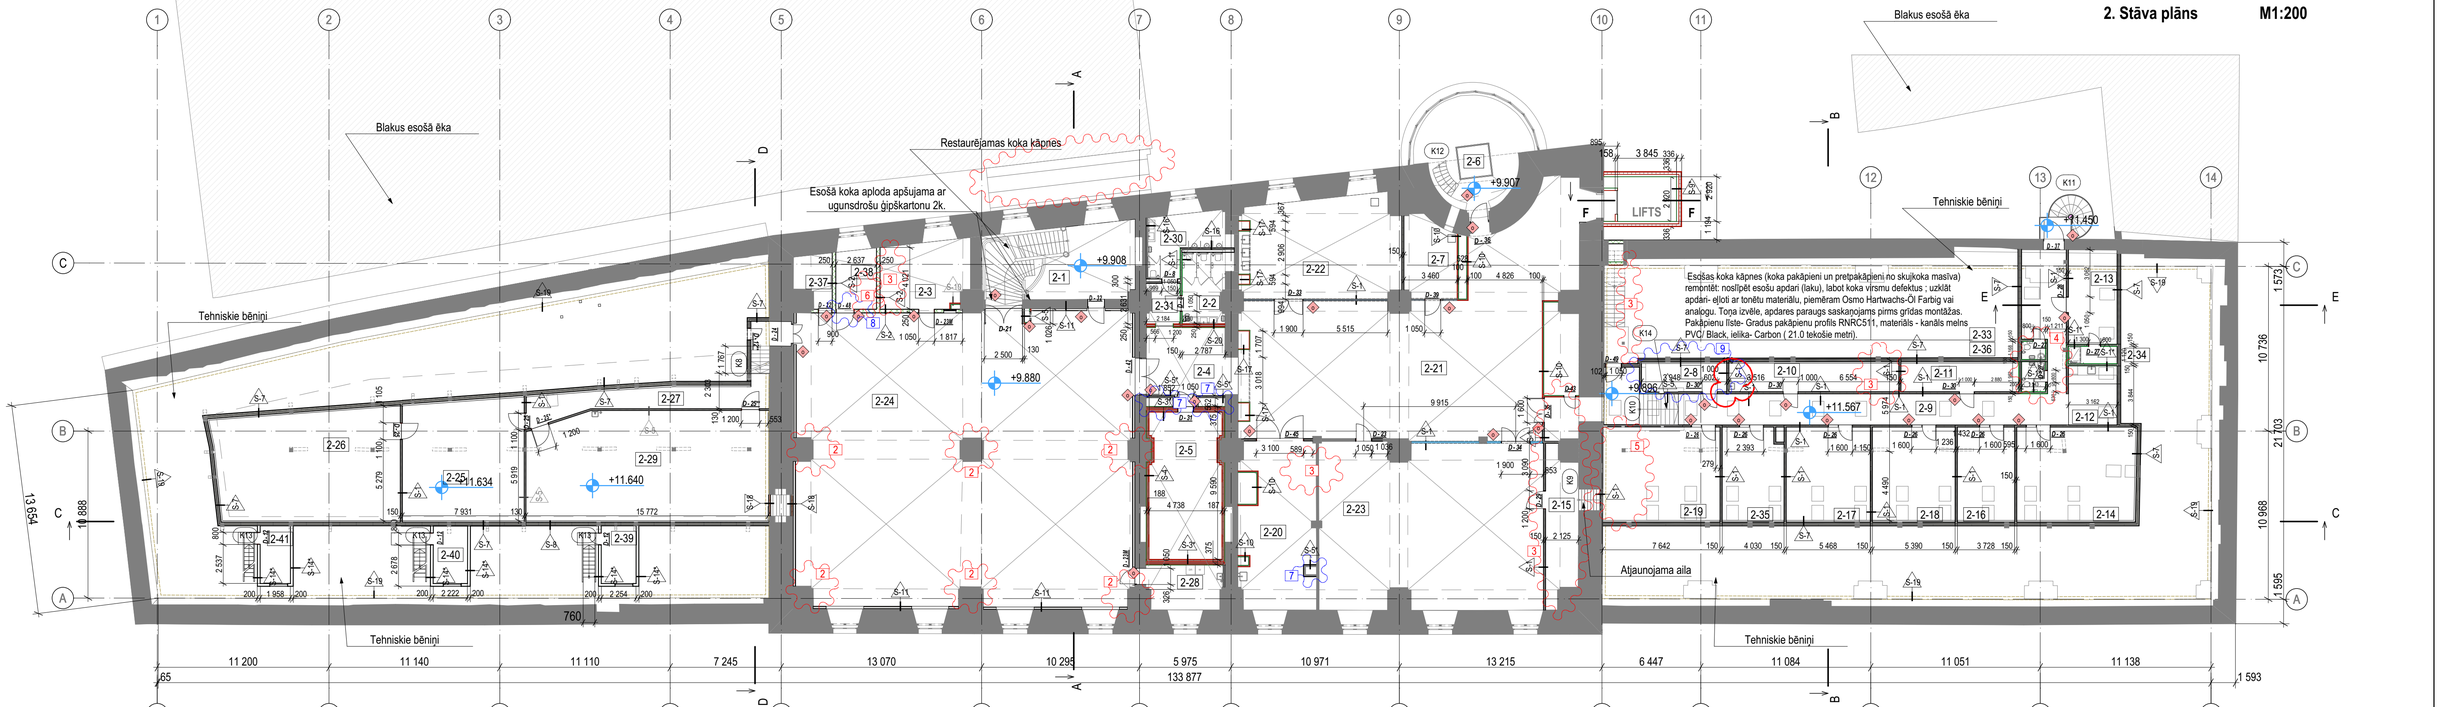

2. Stāva telpu eksplikācija		
Nr.p.k.	Telpu nosaukums	Platība, m2
2-1	Kāpņu telpa	35.28
2-2	WC	12.56
2-3	Vieskuratora darba telpa	24.77
2-4	Vestibils	23.91
2-5	Videomākslas telpa	44.29
2-6	Kāpņu telpa	9.18
2-7	Apsardzes palīgtelpa	17.31
2-8	Servera telpa	10.47
2-9	Gaitenis	95.20
2-10	Palīgtelpa	21.59
2-11	Palīgtelpa	14.70
2-12	Personāla virtuve / atpūtas telpa	12.15
2-13	Darbinieku ģērbtuves	19.49
2-14	Darba telpas	45.00
2-15	Palīgtelpa	19.05
2-16	Darba telpas	21.93
2-17	Darba telpas + zāles vadītājs	32.15
2-18	Darba telpas + ēkas saimnieciskais administrators	31.70
2-19	Apsargiežu telpa	45.50
2-20	Restauratoru telpa	51.42
2-21	Vestibils	219.28

2. Stāva telpu eksplikācija		
Nr.p.k.	Telpu nosaukums	Platība, m2
2-22	Bērnu nodarbību telpa	66.28
2-23	Konferenču zāle	156.44
2-24	Izstāžu telpa	411.64
2-25	Palīgtelpa-videotehnikas novietne	61.61
2-26	Palīgtelpa - materiālu novietne	72.25
2-27	Gaitenis	26.14
2-28	Apkopējas palīgtelpa	14.15
2-29	Tehniskā telpa	109.25
2-30	WC	15.52
2-31	Priekštelpa	5.30
2-33	WC	1.80
2-34	Duša	3.54
2-35	Darba telpas	22.94
2-36	WC	3.01
2-37	Datu telpa	7.21
2-38	Palīgtelpa	10.15
2-39	Gaisa ieņemšanas telpa	7.65
2-40	Gaisa ieņemšanas telpa	7.51
2-41	Gaisa ieņemšanas telpa	6.64
		1 815.95 m²

IZMANTOTIE APZĪMĒJUMI:

ESOŠĀ ĶIEGEĻU MŪRA SIENA AR VĒSTURISKO KAĻĶA APMETUMU (20-30mm)
Ja apmetuma slānis atslāņojies no sienas pamatplaknes vairāk kā 0,5m2 (0,7 x 0,7 m),
tas noņemams visā atslāņojuma laukumā un uznesams no jauna, atbilstoši lapās ARI-25-ARi-26 paredzētajai tehnoloģijai.

JAUNBŪVĒJAMA SIENA

SIENU MARKA

DURVJU MARKA

DURVJU PIEKĻUVES VIRZIENS

TELPU EKSPLIKĀCIJAS NR.

IZSTĀŽU ZĀĻU SIENAS APŠUJAMAS AR FERMACELL LOKSNĒM

PIEZĪMES:

1. Ēkas plānu skatīt kopā ar griezumiem ARi-10, fasādēm ARI-8; ARI-9, sienu griezumiem ARI-12-A un grīdu griezumiem ARi-13-A; ARi-14-A, durvju zīmējumiem ARi-16-A līdz ARi-20-A, kā arī ar projekta ARD daļu.
2. Visi izmēri doti milimetros, visus izmērus precizēt objektā!
3. Zīmējumus nedrīkst mērīt! Lasīt rakstītos izmērus!
4. Būvuzņēmējs ir atbildīgs par dabā esošo izmēru pārbaudi. Atšķirību gadījumā no projekta risinājuma izmaiņas saskaņot ar projekta autoru. Gadījumā, ja konstatētas atkāpes no projekta, par to nekavējoties jāinformē attiecīgās būvprojekta daļas vadītājs.
5. Atsauces uz konkrētiem būvmateriāliem vai piegādātājfirmām, nozīmē tikai šo būvmateriālu vai piegādājamo pakalpojumu kvalitāti un tehnisko rādītāju nepieciešamību, tie var tikt nomainīti ar ekvivalentiem materiāliem ar līdzvērtīgām tehniskām īpašībām, kas atbilst pastāvošajiem Latvijas standartiem, iepriekš saskaņojot ar attiecīgās būvprojekta sadaļas vadītāju;
6. Visas atkāpes no projekta risinājumiem, kā arī no tā izvietošās mezglu un risinājumu papildus detalizācijas izstrādā uzņēmējs, savlaicīgi pirms darbu uzsākšanas vai pasūtījuma izdarīšanas, saskaņojot ar būvprojekta vadītāju un attiecīgās daļas vadītāju.
7. Mezglu vai detaļu izgatavošana, kuru detalizācija nav dota projektā, veicama saskaņā ar izgatavotāja norādījumiem un standartshēmām, kā arī normatīvu prasībām.

B [9]	Labota neprecizitāte, telpai 2-8 nav nepieciešamas ugunsdrošas sienas.	Indra Valtere	11.02.2026.
B [8]	Mainīts durvju vēršanās virziens, jo piekļuves kontrole projektēta durvju labajā pusē.	Indra Valtere	17.12.2025.
B [7]	Veidota ugunsdroša šahtsiena, lai nebūtu vent. caurulē jāiebūvē ugunsdrošs vārsts.	Indra Valtere	16.12.2025.
A [6]	Noņemts šahtas apšuvums, AVK tīklu izvietojuma dēļ šahtas izmērs palielinātos neproporcionāli liels tik mazai palīgtelpai.	Laila Ruža	28.05.2025.
A [5]	Saskaņā ar Pasūtītāja vēlmi, netiek plānota telpa tulkiem	Indra Valtere	21.01.2025.
A [4]	Saskaņā ar telpu faktiskajiem izmēriem, mainīts plānojums	Indra Valtere	21.01.2025.
A [3]	Saskaņā ar inženiertīklu trasēm, mainīts plānojums	Indra Valtere	10.05.2025.
A [2]	Saskaņā ar Pasūtītāja vēlmi, izņemti S-1 apšuvumi ap kolonnām	Indra Valtere	10.05.2025.
A	Saskaņā ar "purikļu mākoni" un situāciju dabā, demontāžas apjomi precizēti, izņemti no lapas ARi-4, parādīti jaunveidotā lapā ARi-37	Indra Valtere	10.05.2025.
Rev. apz.	Izmaiņu apraksts, pamatojums	Izmaiņas veica	Datums

BŪVNIECĪBAS IEROSINĀTĀJS:
VAS "VALSTS NEKUSTAMIE ĪPAŠUMI"
Talejas iela 1, Rīga, LV - 1026
reģ.Nr.40003294758

BŪVPROJEKTA IZSTRĀDĀTĀJS:
ARHSTADIJA
ARHITEKTU BIROJS
PĒRNAVAS IELA 42, RĪGA, LV-1009
BŪVKOMERSANTA REĢ.NR. 19226-R
REĢ.NR. 40003457772

OBJEKTS:
izmaiņas pie būvprojekta
IZSTĀŽU ZĀLES "ARSENĀLS" PĀRBŪVES PROJEKTS
TORŅA IELĀ 1, RĪGA
kadastra Nr. 0100 008 0055

DAĻA: **ARHITEKTŪRA** — MARKA: **AR**

RASĒJUMA NOSAUKUMS: 2. Stāva plāns

B.P.V. **Aldis Polis**	12.02.2026	sert.Nr.1-00572	Mērogs 1:200	STADIJA: **BP**	
B.P.D.V. **Aldis Polis**	12.02.2026	sert.Nr.1-00572	DATUMS: 12.02.2026	LAPA: ARi-4-B	IZM.: B
Arhitekte **Elita Pole**	12.02.2026	sert.Nr.1-00012		LAPU SKAITS:	
Arhitekte **Indra Valtere**	12.02.2026	sert.Nr.1-00804			
Arhitekte **Laila Ruža**	12.02.2026				

Līguma/arhīva Nr. **ARS 1_13/2024**

ŠIS RASĒJUMS TIEK IZSNIEGTS TIKAI KĀ PROJEKTA DOKUMENTĀCIJAS SASTĀVDAĻA. SAŅĒMĒJS PIEKRĪT NEPAVAIROTUN NEIZMAINĪT ŠO RASĒJUMU VAI TĀ DAĻAS BEZ PROJEKTĒTĀJA PIEKRIŠANAS. SAŅĒMĒJS PIEKRĪT, KA ŠIS RASĒJUMS NAV IZMANTOJAMS CITU OBJEKTU PROJEKTĒŠANAI UN CELTNIECĪBAI BEZ SASKAŅOŠANAS AR SIA "ARH STADIJA".

Fails "IZ_4varnais" revidēts 12.02.2026 14:43